


	型名	基礎柱		偏
		Dx	Dy	
		mm	mm	
1'C1	HP4530H	0	0	
1'C2	SP303H	0	0	
1'C3	SP303H	0	0	
1'C4	SP301H	0	0	
1'C5	HPS6030H	0	0	
1'C6	HP6030H	0	0	
P1				
P1A				
P2				

C1:	800x940	D850
C2:	740x740	D850
C3:	740x740	D850
C4:	680x680	D750
C5:	1,090x810	D1000
C6:	1,100x840	D1000

伏図(1)

特記なき限り下記による

1. 柱BPL下端 礎柱天端+50とする

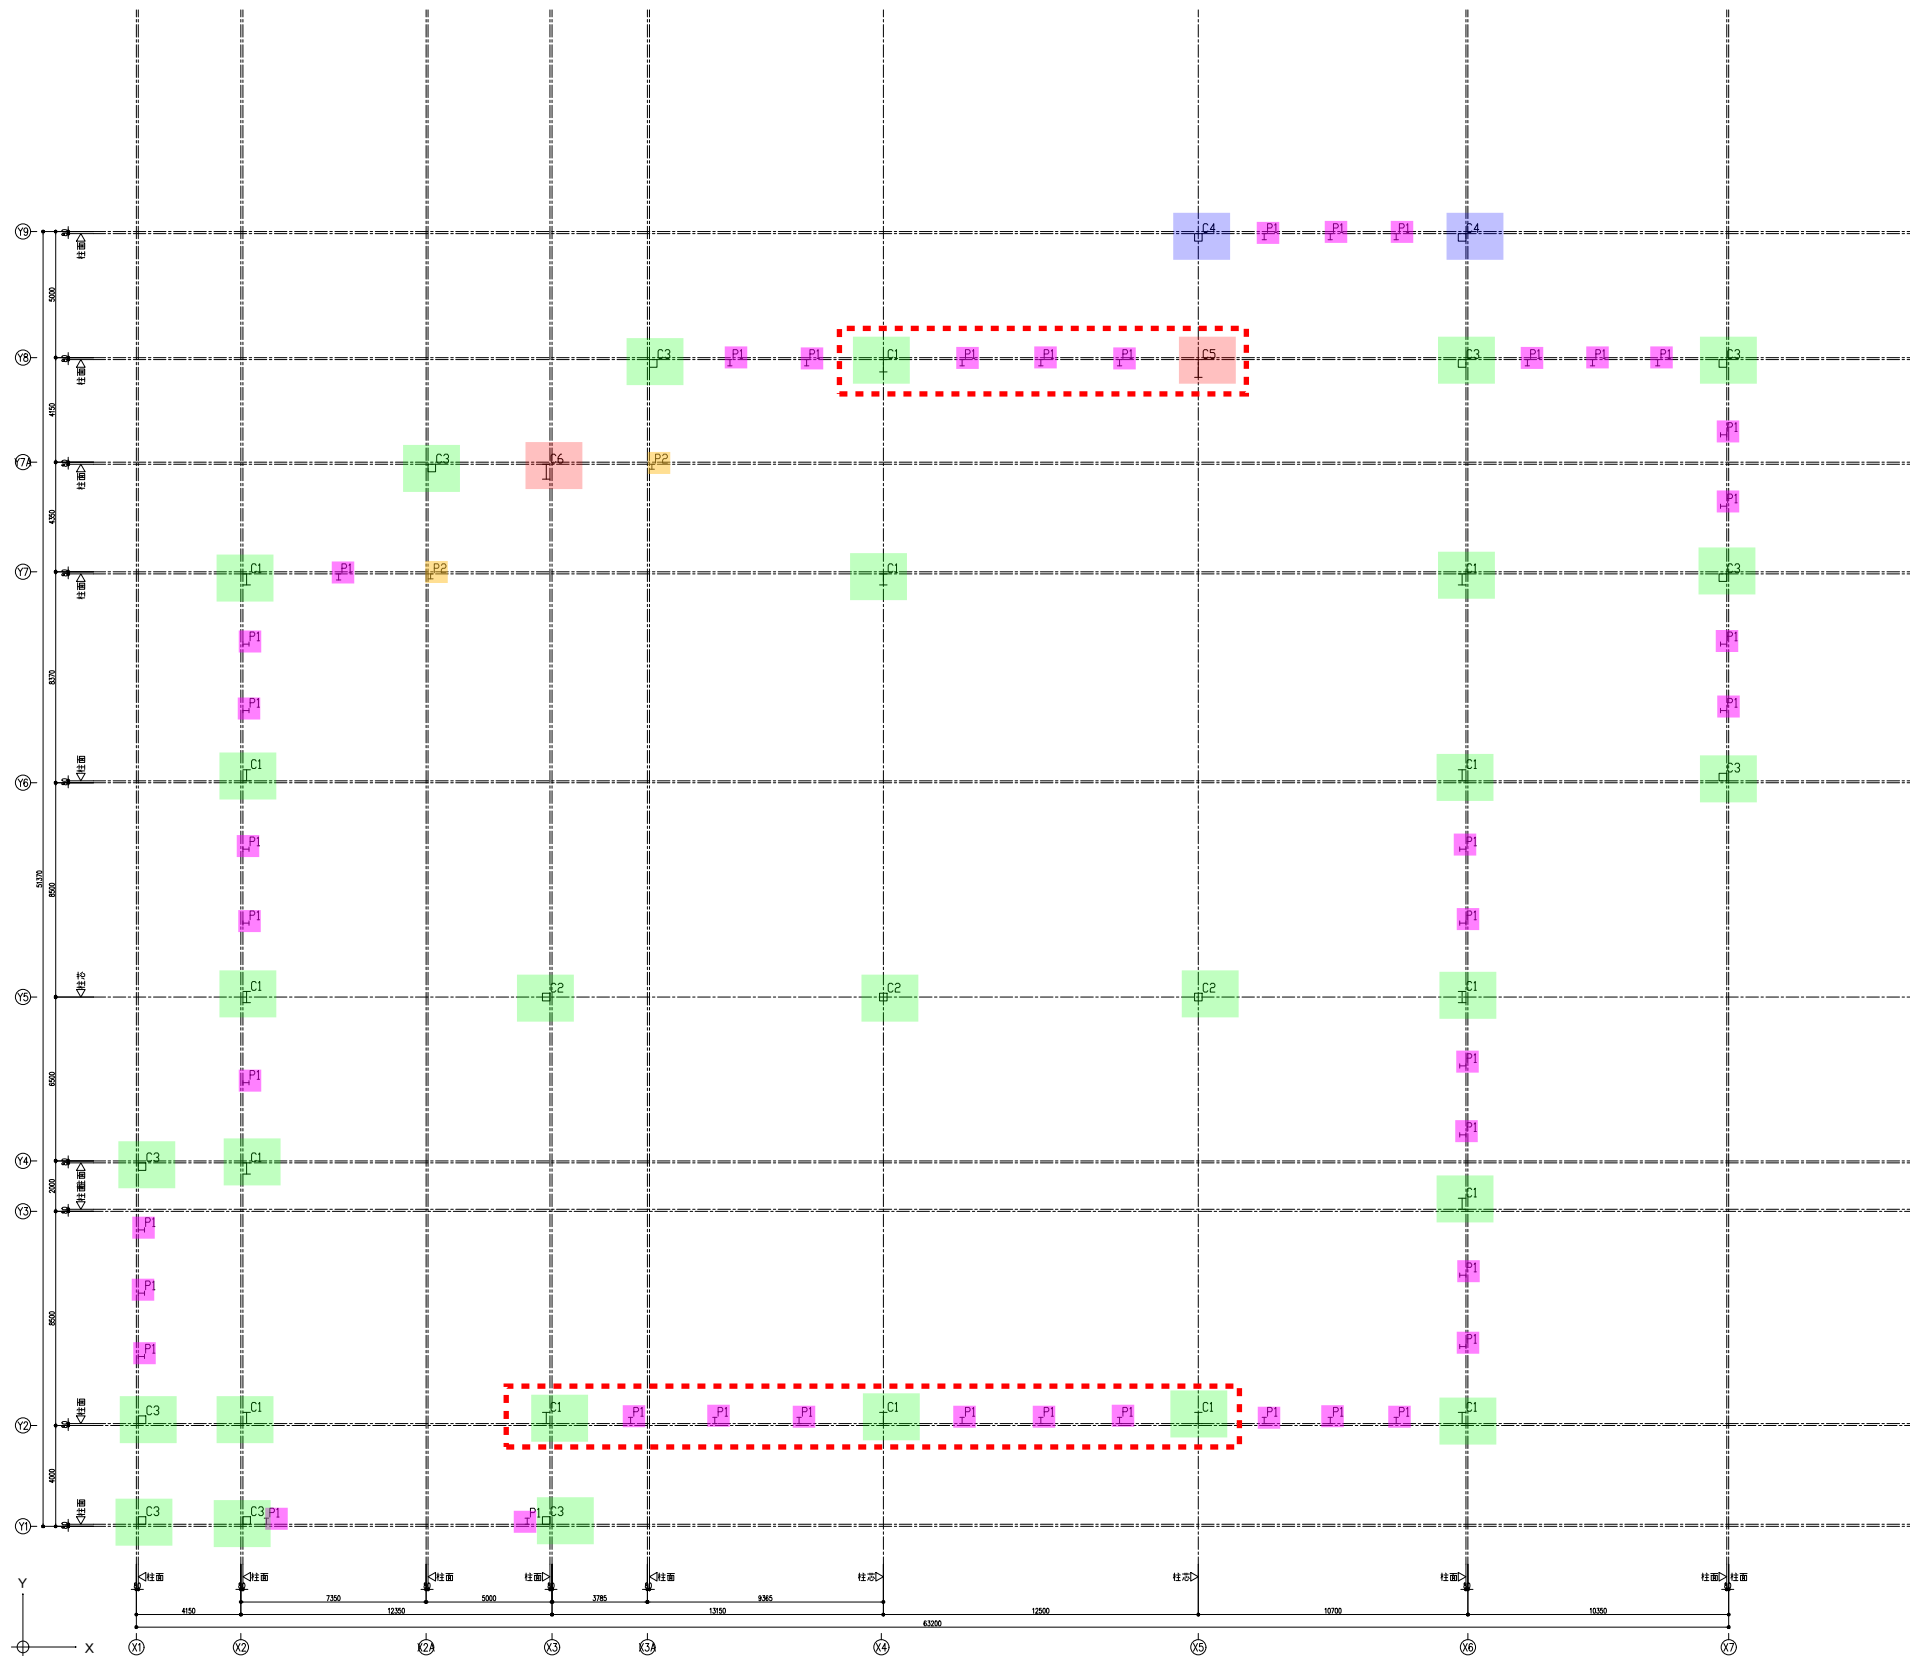


	(仮称) 大阪市住之江区南港北2丁目 計画	株式会社 日 企 設 計						No. 図 面 番 号
		S - 17						
	伏図(1)	一級建築士事務所 登録番号(予)10572号	統括	部長		課長	担当	製作年月日
	S=1:200 (A1) S=1:400 (A3)	一級建築士第159568号 森田俊和						2025年 4月 14日



適用H形鋼 サイズ	内法一定	
	H-434×299×10×15	
	H-440×300×11×18	
	外法一定	
	*	
アンカーボルト	4-M48	
ベースプレート	710×570×55	
柱形断面	940×800 (1010×1000)※ ¹	
主筋	16-D25	
帯筋	D13@125	
最小コンクリート強度	21N/mm ²	
回転剛性	強軸方向	121,000kN・m/rad
	弱軸方向	64,000kN・m/rad

※1：柱形断面の()内寸法は、最大寸法を示します。


曲げ耐力図

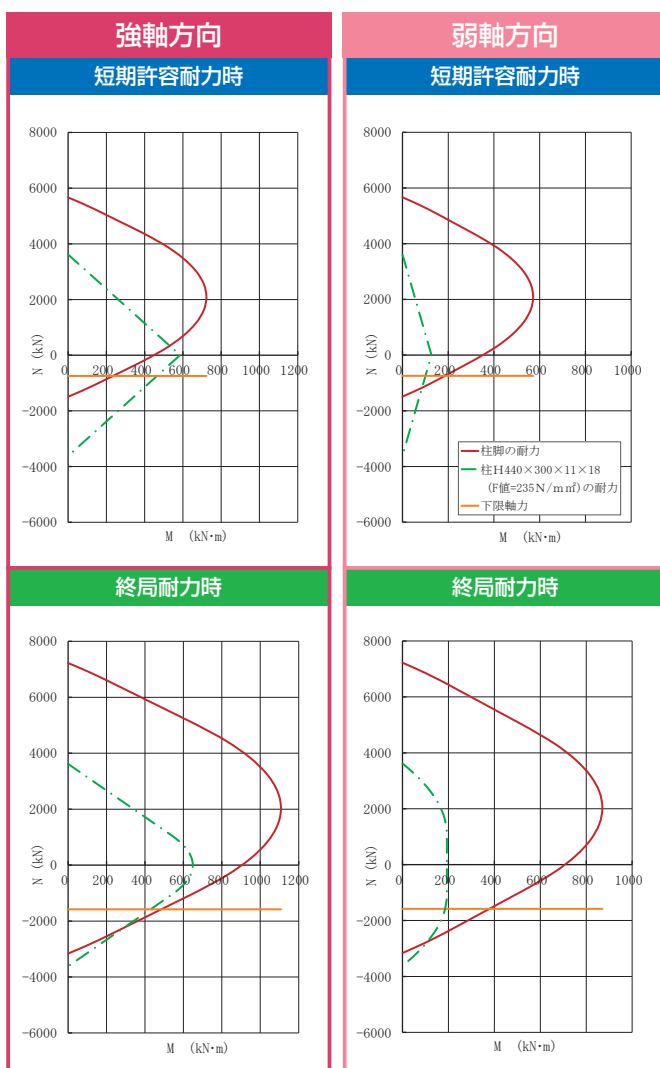

標準形状

(単位:mm)

C1: 800x940 D850

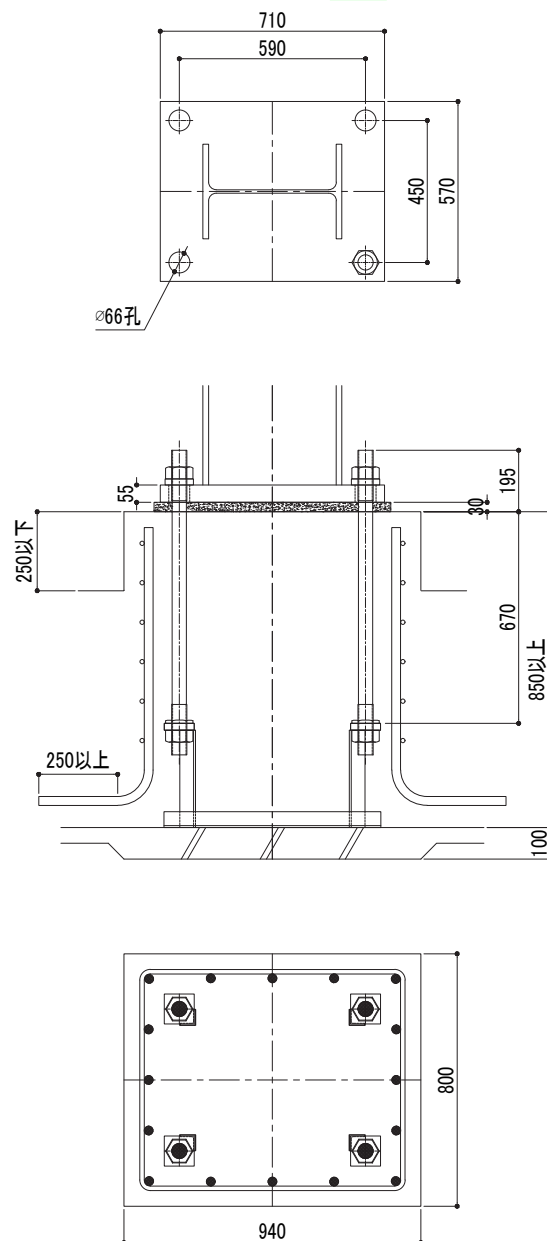

下限軸力及びBOPせん断耐力

(単位:kN)

強軸方向	下限軸力	BOPせん断耐力	弱軸方向	下限軸力	BOPせん断耐力
短期許容耐力時	-745	299	短期許容耐力時	-745	225
終局耐力時	-1,581	399	終局耐力時	-1,581	301

注意事項

- 杭基礎の場合の基礎高さは、最低高さに杭出寸法を加算して下さい。
- 下限軸力、BOPせん断耐力の運用については、設計ハンドブックを参照して下さい。
- 柱脚運用に際して、その他の注意事項については、P2を参照して下さい。




鋼管サイズ	□ 300	
適用鋼管	F値=235	t≤16
	F値=275・295	t≤16
	F値=325	t≤12
アンカーボルト	8-M42	
ベースプレート	530×530×45	
柱形断面	740×740 (840×840)*1	
主筋	24-D22	
帯筋	D13@100	
最小コンクリート強度	21N/mm ²	
回転剛性	85,000kN・m/rad	

※1：柱形断面の()内寸法は、最大寸法を示します。

標準形状

(単位:mm)

C2: 740x740 D850 C3: 740x740 D850

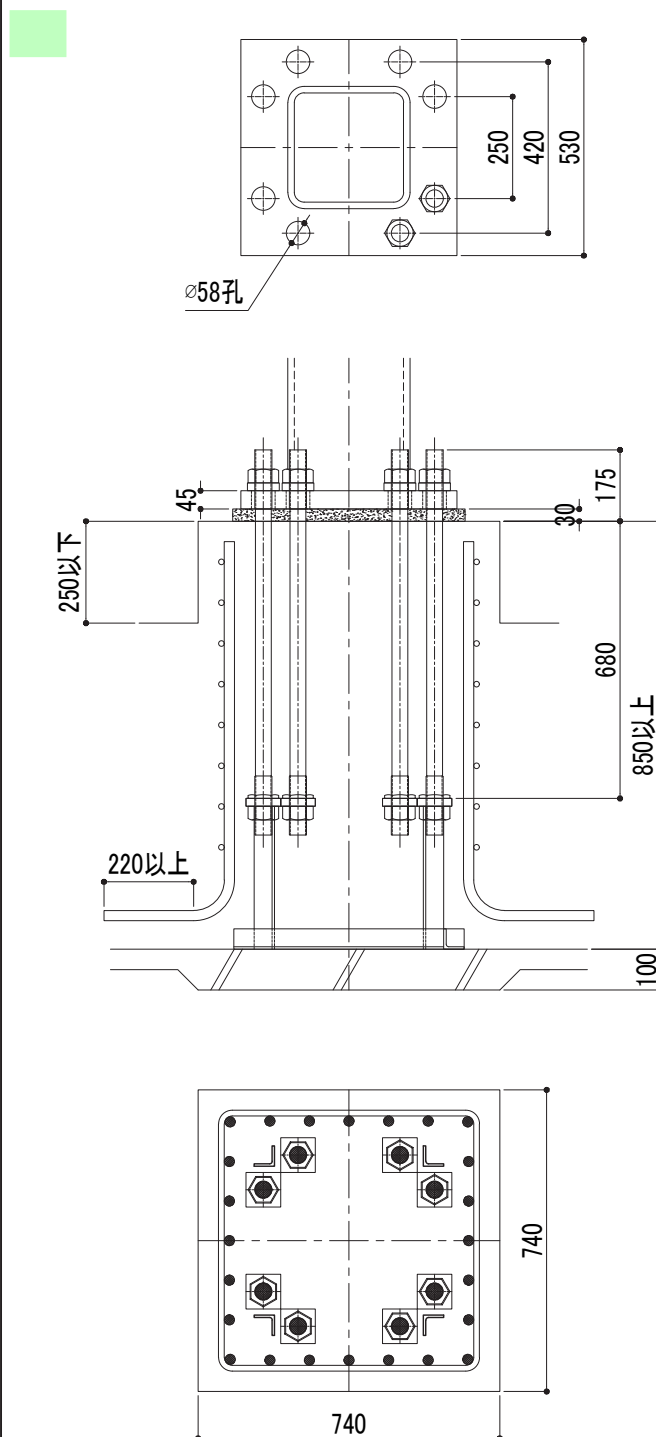


曲げ耐力図

短期許容耐力時

(単位:kN)


下限軸力 -905 BOPせん断耐力 143

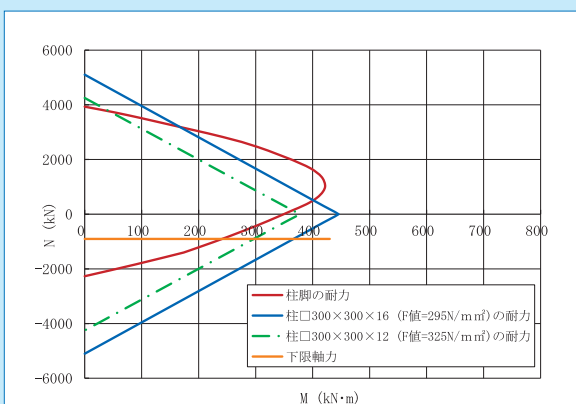

終局耐力時

(単位:kN)

下限軸力 -2,343 BOPせん断耐力 191

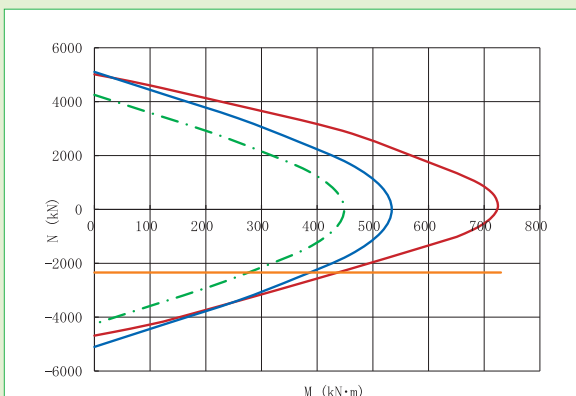

注意事項

- 杭基礎の場合の基礎高さは、最低高さに杭出寸法を加算して下さい。
- 下限軸力、BOPせん断耐力の運用については、設計ハンドブックを参照して下さい。
- 柱脚運用に際して、その他の注意事項については、P2を参照して下さい。




鋼管サイズ	□ 300	
適用鋼管	F値=235	t≤9
	F値=275・295	t≤9
	F値=325	*
アンカーボルト	4-M42	
ベースプレート	480×480×36	
柱形断面	680×680 (840×840)*1	
主筋	16-D22	
帯筋	D13@100	
最小コンクリート強度	21N/mm ²	
回転剛性	56,000kN・m/rad	

※1：柱形断面の()内寸法は、最大寸法を示します。

標準形状

(単位:mm)

C4: 680x680 D750

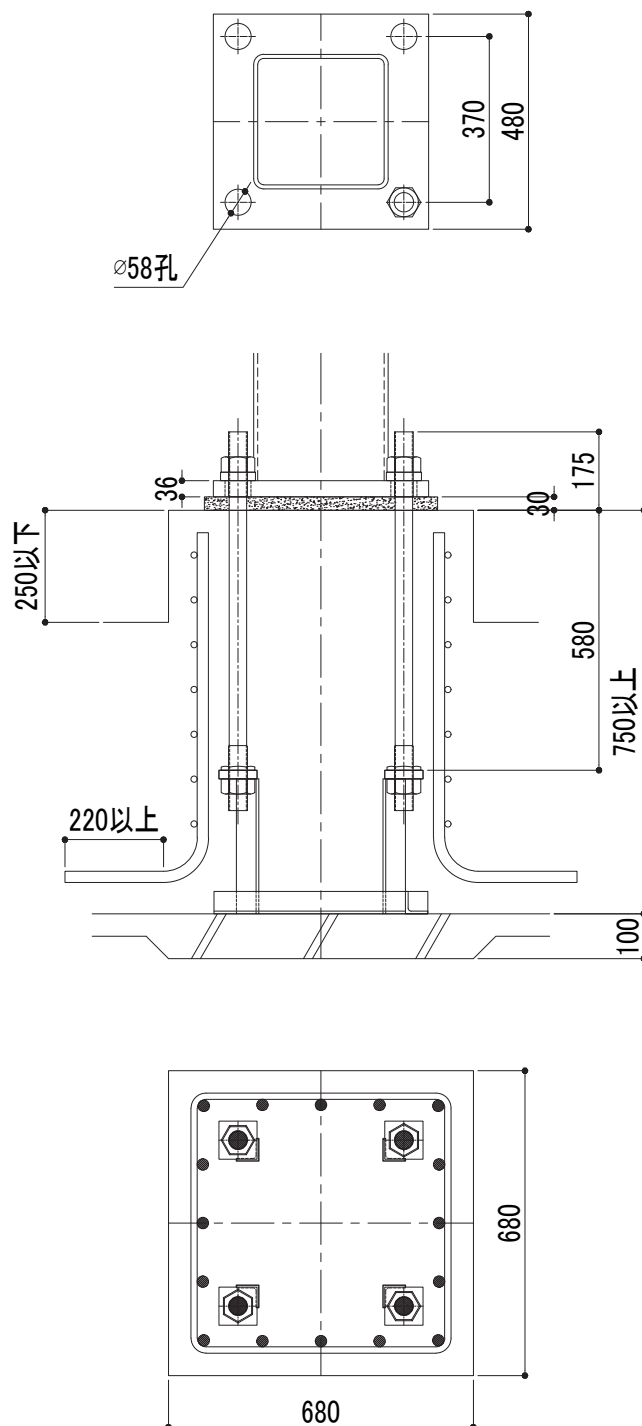


曲げ耐力図

短期許容耐力時

(単位:kN)


下限軸力 -567 BOPせん断耐力 117

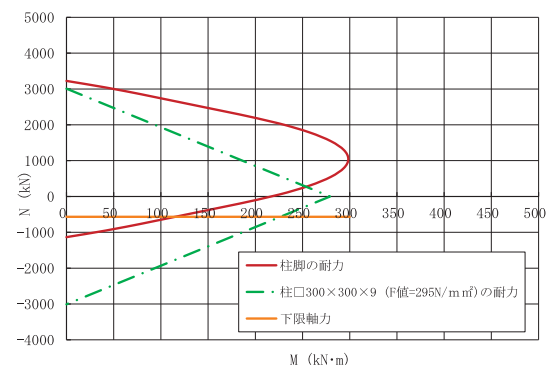

終局耐力時

(単位:kN)

下限軸力 -1,203 BOPせん断耐力 156

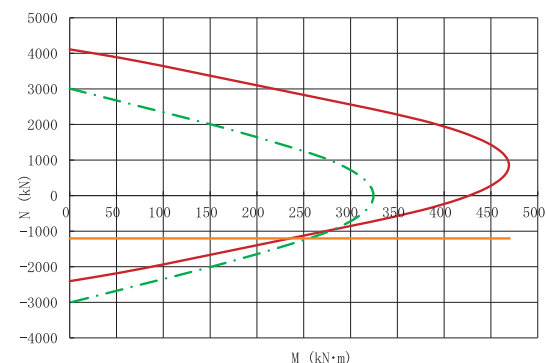

注意事項


- 杭基礎の場合の基礎高さは、最低高さに杭出寸法を加算して下さい。
- 下限軸力、BOPせん断耐力の運用については、設計ハンドブックを参照して下さい。
- 柱脚運用に際して、その他の注意事項については、P2を参照して下さい。



適用H形鋼 サイズ	内法一定	
	H-582×300×12×17	
	H-588×300×12×20	
	外法一定	
アンカーボルト	8-M48	
	ベースプレート	
	860×580×70	
	柱形断面	
主筋	1090×810 (1260×1260)※1	
	26-D25	
	帯筋	
	D13@100	
最小コンクリート強度	21N/mm ²	
	回転剛性	強軸方向
		366,000kN・m/rad
	弱軸方向	90,000kN・m/rad


※1：柱形断面の()内寸法は、最大寸法を示します。

曲げ耐力図

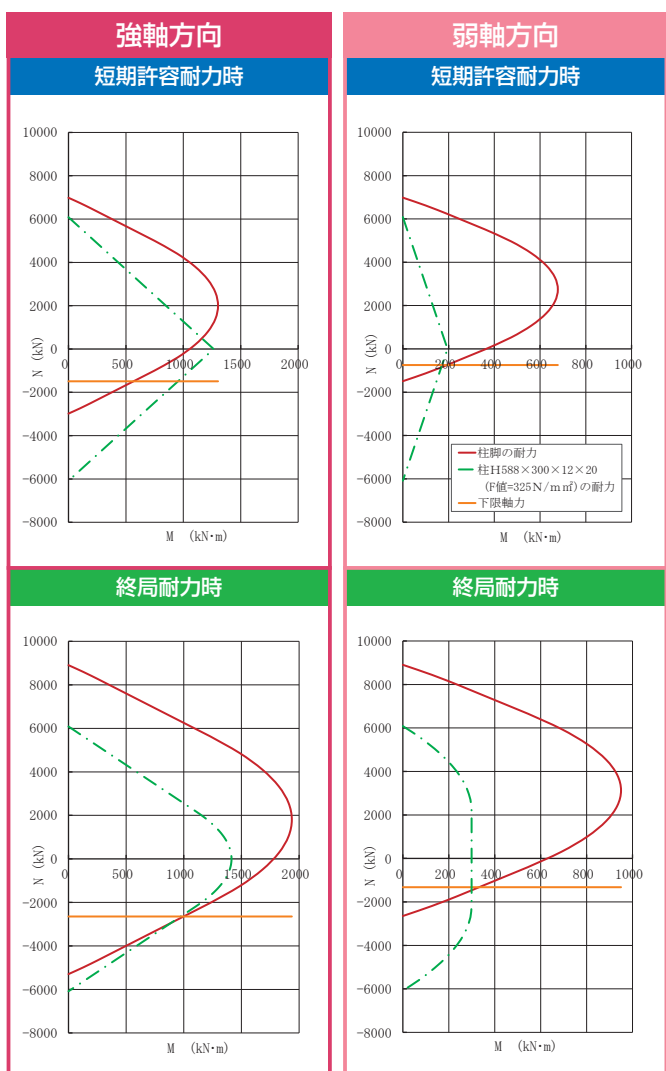


標準形状

(単位:mm)

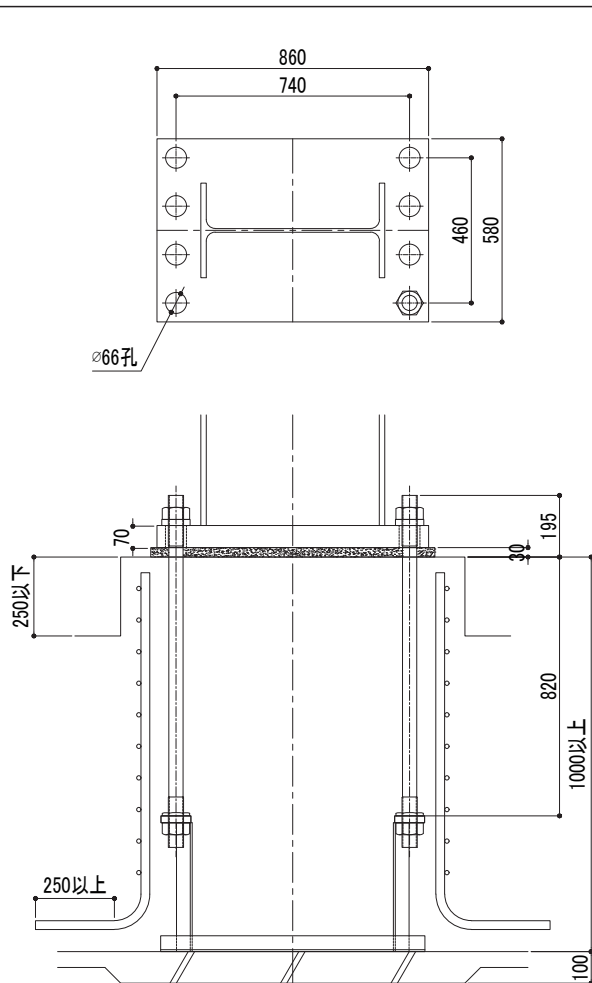

C5: 1,090x810 D1000

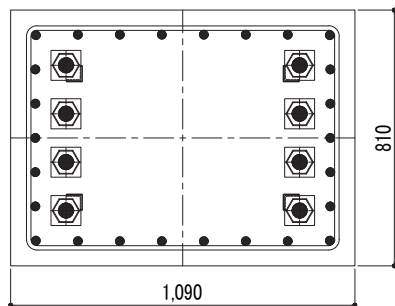

下限軸力及びBOPせん断耐力

(単位:kN)

強軸方向	下限軸力	BOPせん断耐力	弱軸方向	下限軸力	BOPせん断耐力
短期許容耐力時	-1,491	359	短期許容耐力時	-745	257
終局耐力時	-2,648	478	終局耐力時	-1,324	343

注意事項


- 杭基礎の場合の基礎高さは、最低高さに杭出寸法を加算して下さい。
- 下限軸力、BOPせん断耐力の運用については、設計ハンドブックを参照して下さい。
- 柱脚運用に際して、その他の注意事項については、P2を参照して下さい。



適用H形鋼 サイズ	内法一定	
	H-582×300×12×17	
	H-588×300×12×20	
	外法一定	
	H-600×300×12×19	
		H-600×300×12×22
アンカーボルト	6-M48	
ベースプレート	860×610×60	
柱形断面	1100×840 (1210×940)※ ¹	
主 筋	18-D25	
帯 筋	D13@100	
最小コンクリート強度	21N/mm ²	
回転 剛性	強軸方向	288,000kN・m/rad
	弱軸方向	88,000kN・m/rad


※ 1：柱形断面の()内寸法は、最大寸法を示します。

曲げ耐力図

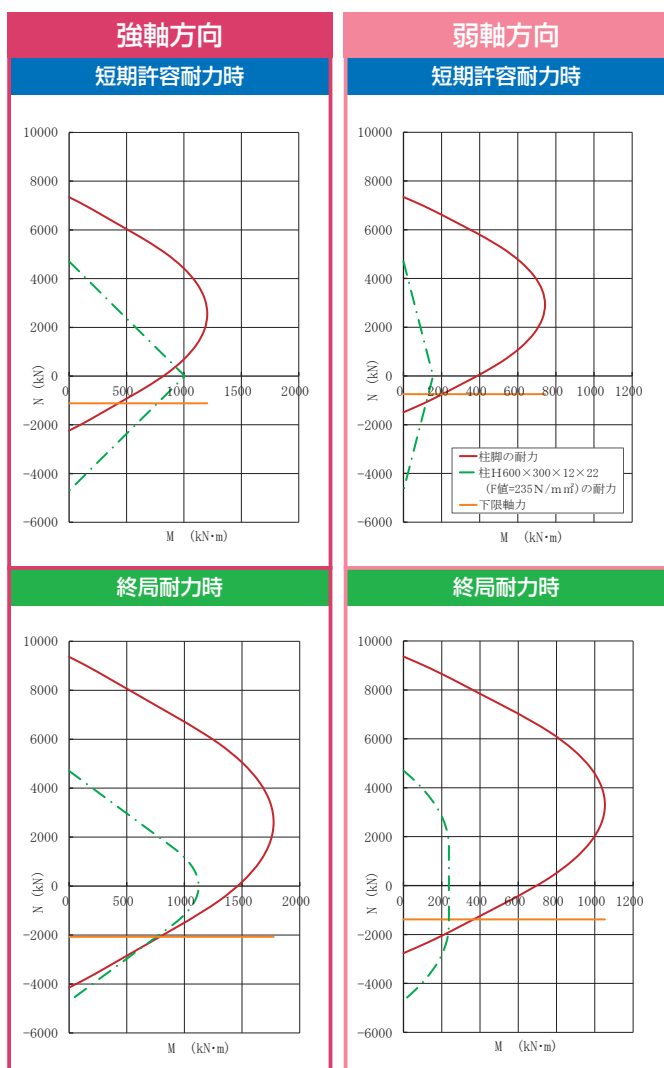

標準形状

(単位:mm)

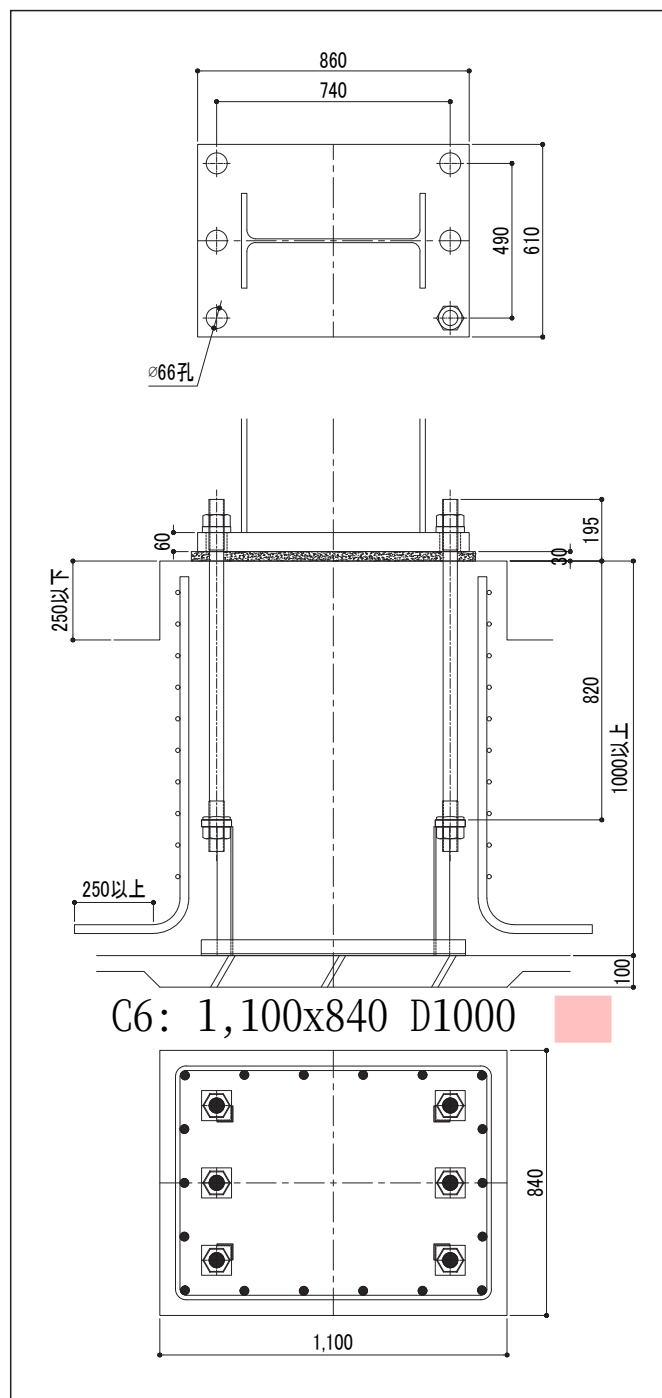

下限軸力及びBOPせん断耐力

(単位:kN)

強軸方向	下限軸力	BOPせん断耐力	弱軸方向	下限軸力	BOPせん断耐力
短期許容耐力時	-1,118	404	短期許容耐力時	-745	297
終局耐力時	-2,072	539	終局耐力時	-1,382	396

注意事項

- 杭基礎の場合の基礎高さは、最低高さに杭出寸法を加算して下さい。
- 下限軸力、BOPせん断耐力の運用については、設計ハンドブックを参照して下さい。
- 柱脚運用に際して、その他の注意事項については、P2を参照して下さい。