


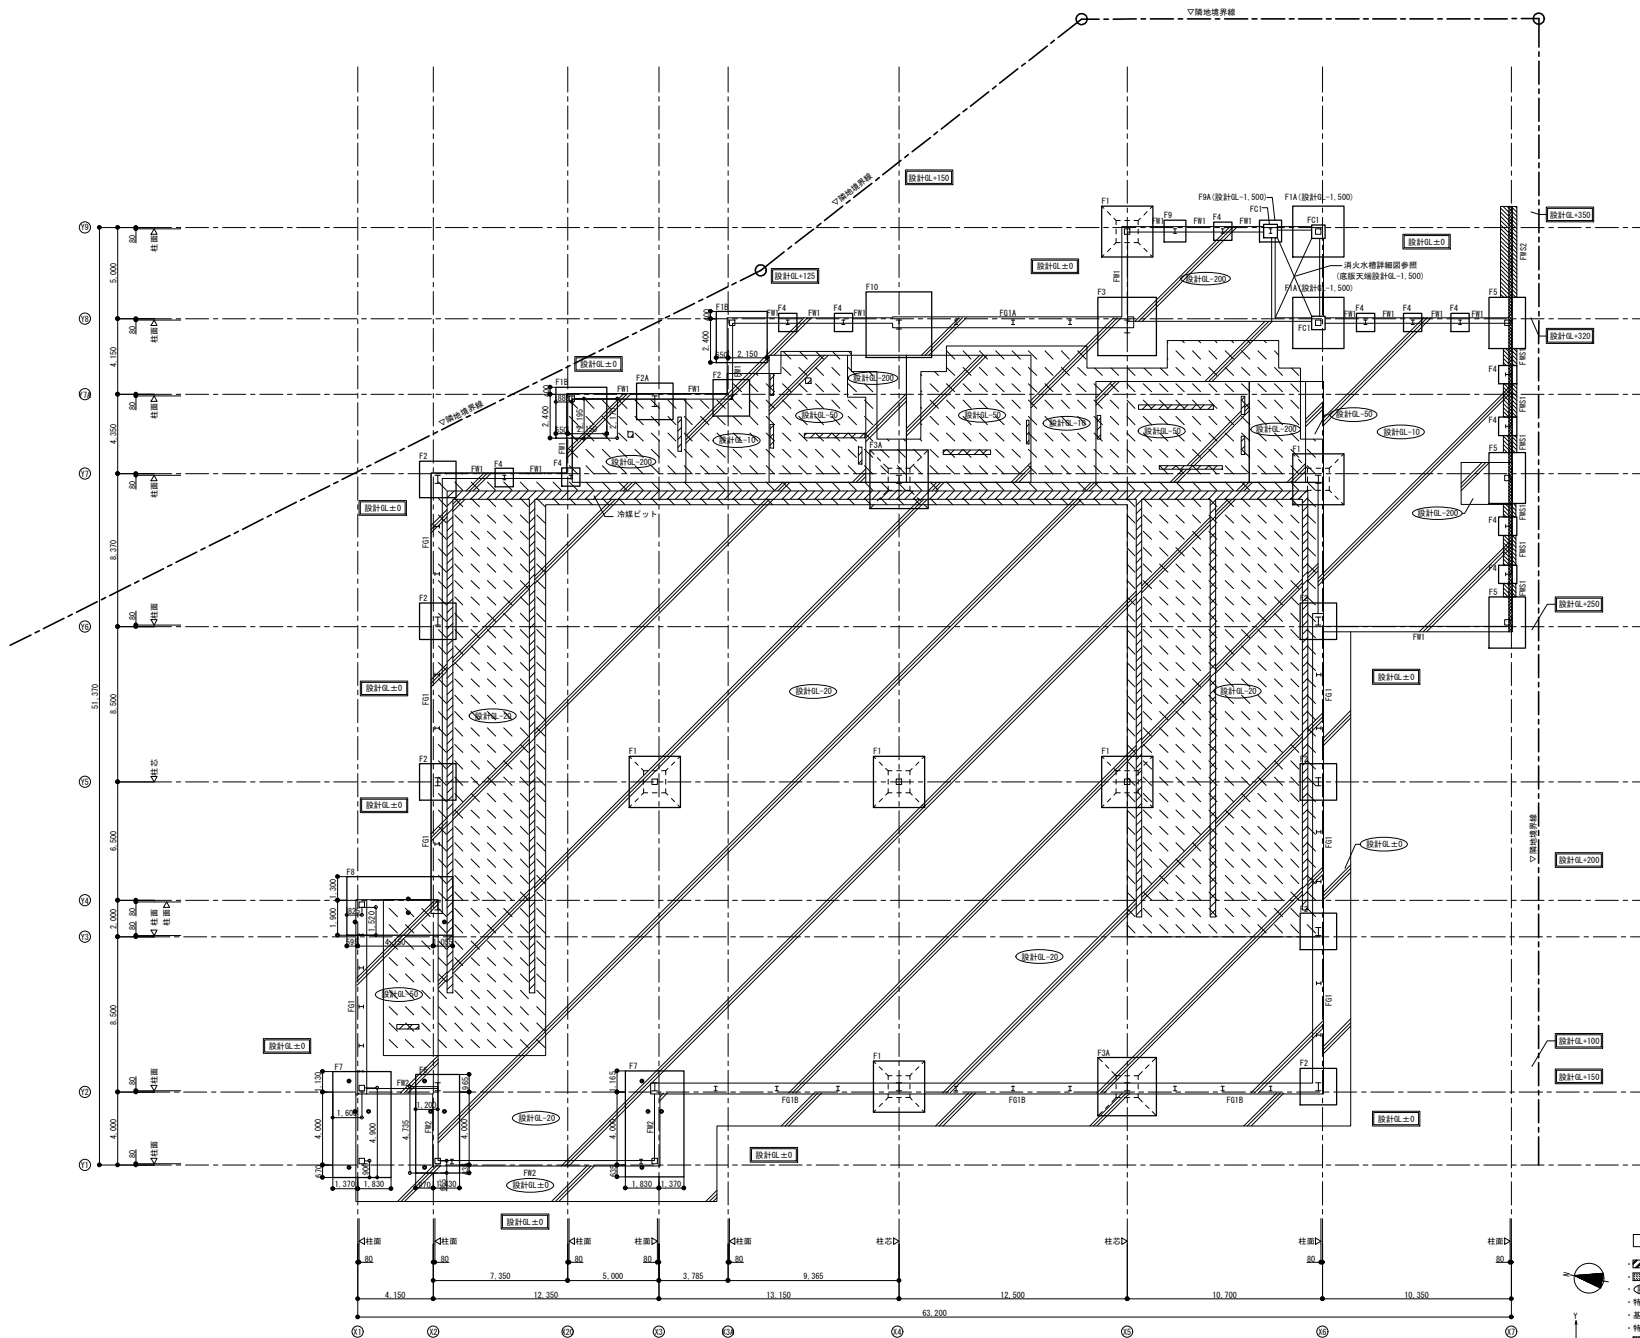

- 基礎状況
- は土間コンクリート (t=150, D13@200 シングル配筋) の範囲を示す。
 - は土間下から設計値-500まで砕石又は改良断層土埋戻しとする。
 - は土間天端高さを示す。
 - 特記無き基礎配置は、柱芯からの振り分けとする。
 - 特記無き基礎天端高さは、設計値-500とする。
 - 特記無き基礎天端高さは、設計値-500とする。
 - はビットの範囲を示す。
 - は埋設物存在部の範囲を示す。
 - は埋設物PSの範囲を示す。
 - は、外構土高さを示す。

株式会社タウチ建設一級建築士事務所
一級建築士事務所 広島県広島市南区24(1)第5643号
一級建築士大田 登雄 第303331号
構造設計一級建築士 第7249号 沖本 隆平

(仮称) ラ・ムー南港店 新築工事

TNF工法 (特許工法) 基礎伏図

S=1:150 (A1)
S=1:300 (A3)

株式会社 日企設計

一級建築士事務所	統括	部長	課長	担当
登録番号(リ)10572号				
一級建築士大田 登雄 第303331号				
構造設計一級建築士 第7249号 沖本 隆平				

図面番号
S - 13

製作年月日
2025年 月 日